


DACHAUFMASS — HALLE C4

Dachgeometrie für PV-Modulmontage (dachparallele Montage)

GRUNDRISS


M 1:600

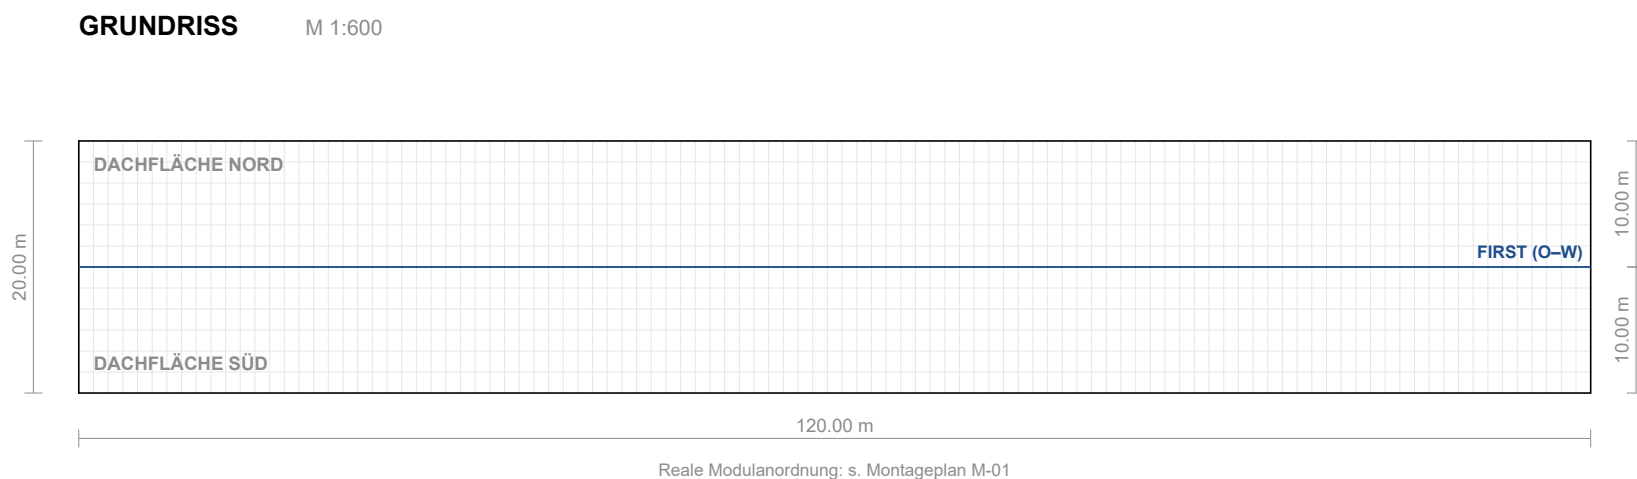

Reale Modulanordnung: s. Montageplan M-01

QUERSCHNITT A-A

M 1:150

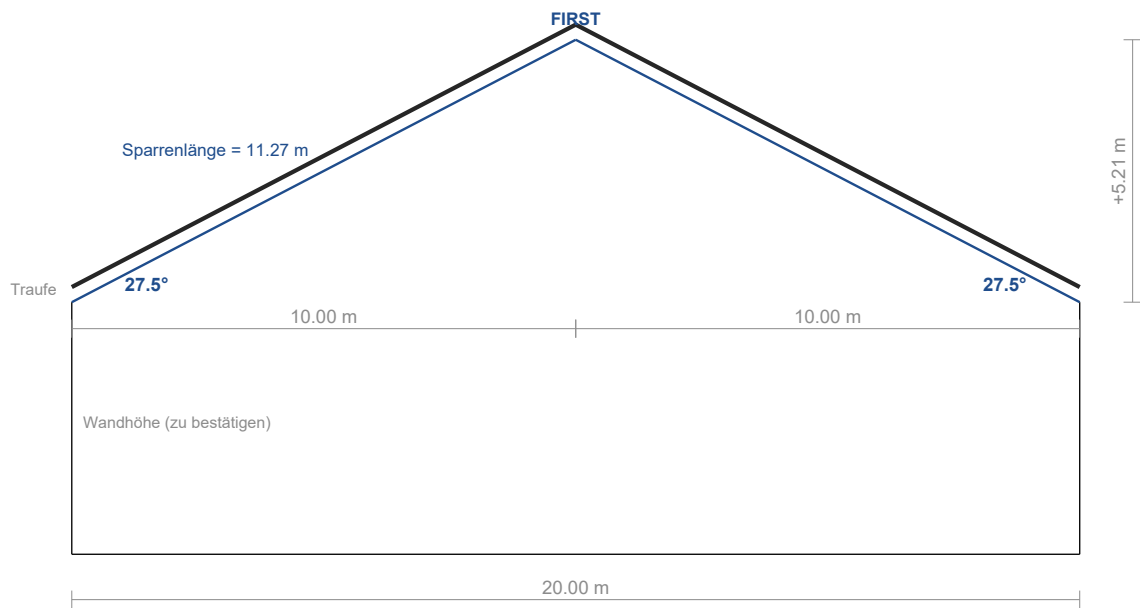

TECHNISCHE ANGABEN

Dachtyp:	Satteldach, Neigung 27.5°
Dacheindeckung:	Faserzement-Wellplatten (Typ Eternit)
Montagesystem:	Stockschrauben + Schienen, dachparallel
Grundrissmaße:	120.00 × 20.00 m
Sparrenlänge:	11.27 m (Projektion 2×10.00 m)
Firsthöhe:	+5.21 m über Traufe
Dachfläche:	≈ 2706 m² (2 Flächen)
Ausrichtung:	First O–W; Flächen Nord / Süd
PV-Module:	C4-Süd D66 710W · C4-Nord H48 450W
Modulanzahl:	1010 Stk ≈ 556 kWp (s. Montageplan M-01)

DACHAUFBAU / MERKMALE:

- Platte: Faserzement-Wellplatte (Asbestzement), Dicke 8 mm
- Unterkonstruktion: Holzpfeilen
- Zustand: gut

Befestigung: Stockschraube in Pfetten/Tragkonstruktion,
mit Dichtung für Faserzement-Wellplatten.

! Richtmaße — vor Ort durch Aufmaß zu bestätigen.

Arbeitsdokument; Prüfung durch autorisierten Planer erforderlich.

BAUHERR:
S.C. RED INTERNET SALES S.R.L.

PROJEKT:
Autonome PV-Anlage:
Energie der Zukunft für ein nachhaltiges Rumänien

SMIS-Code 332037 | ≈ 1 MWp

Standort: Albești (Schäßburg), Kreis Mureș

PLANINHALT:

HALLE C4

Dachgeometrie-Aufmaß
für PV-Modulmontage

Phase: informativ
Erstellt: Geprüft:

MASSTAB: **1:600 / 1:150**

DATUM: 07.2026

FORMAT: A3

BLATT: **A-01**