


PLAN DE MONTAJ PANOURI FOTOVOLTAICE — HALA C4

Poziționare module pe cele 2 fețe (eficiente pe sud) — instalat ≤ 1 MW, coplanar

VEDERE ÎN PLAN — DISPUNERE MODULE

sc. 1:600


FAȚA NORD — STP450S-H48 450W: 618 buc (103×6 portret)

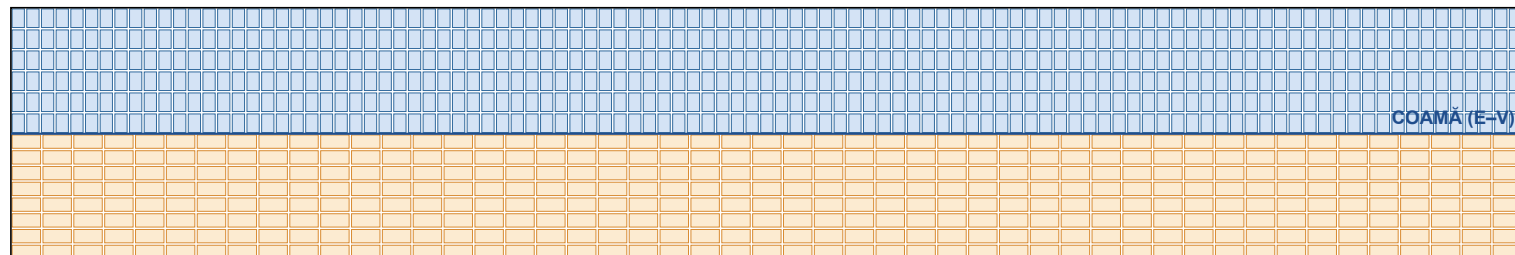

FAȚA SUD (eficiente) — STP710S-D66 710W: 392 buc (49×8 landscape)

SECȚIUNE A-A

1:150

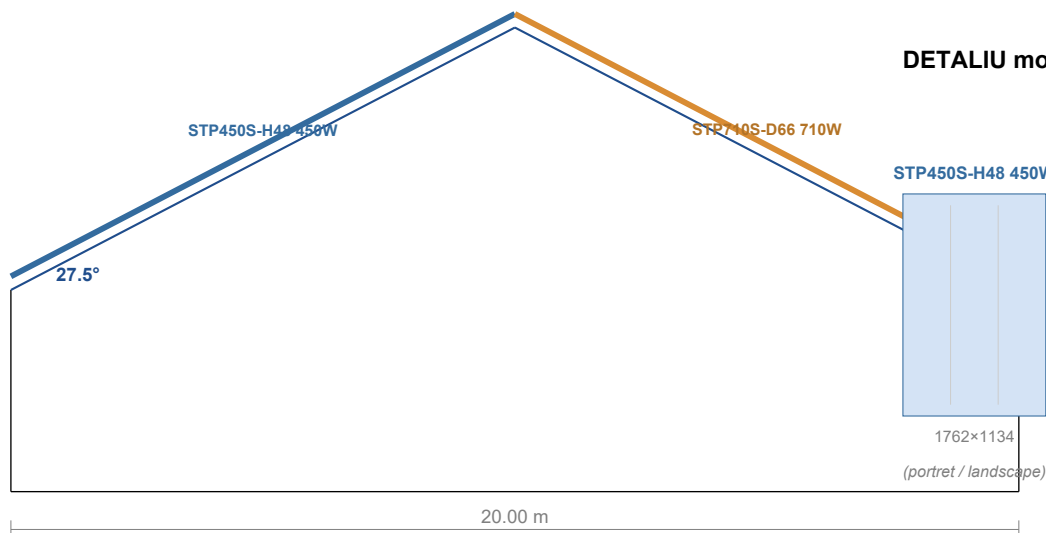

DETALIU module (1:60)

STP450S-H48 450W

1762×1134
(portret / landscape)

STP710S-D66 710W

2384×1303

N



LEGENDĂ / CANTITĂȚI

Acoperiș: 120×20 m · pantă 11,27 m @27,5°

FAȚA NORD:

STP450S-H48 450W · 618 buc · 278 kWp

FAȚA SUD (eficiente):

STP710S-D66 710W · 392 buc · 49×8 landscape · 278 kWp

TOTAL hala: 1010 buc $\approx$ 556 kWp

Fixare:

Prezoane fibrociment + șine

C4 + C6: 1937 buc $\approx$ 989 kWp (≤ 1 MW)

! Cantități/dispunere orientative — de confirmat prin releveu și calcul static.

Document de lucru; verificare de proiectant autorizat.

BENEFICIAR:

S.C. RED INTERNET SALES S.R.L.

PROIECT:

Panouri Fotovoltaice Autonome — cod SMIS 332037

≤ 1 MWp

Amplasament: Albești (Sighișoara), jud. Mureș

OBIECT PLANȘĂ:

HALA C4

Plan de montaj module FV

Faza: informativ
Întocmit: Verificat:

SCARA:

1:600 / 1:150

DATA:

08.2026

FORMAT:

A3

PLANȘA:

M-01


PV MODULE MOUNTING PLAN — HALL C4

Module positioning on the 2 faces (efficient on south) — installed ≤ 1 MW, coplanar

LAYOUT PLAN — MODULE ARRANGEMENT

scale 1:600

NORTH FACE — STP450S-H48 450W: 618 pcs (103×6 portrait)

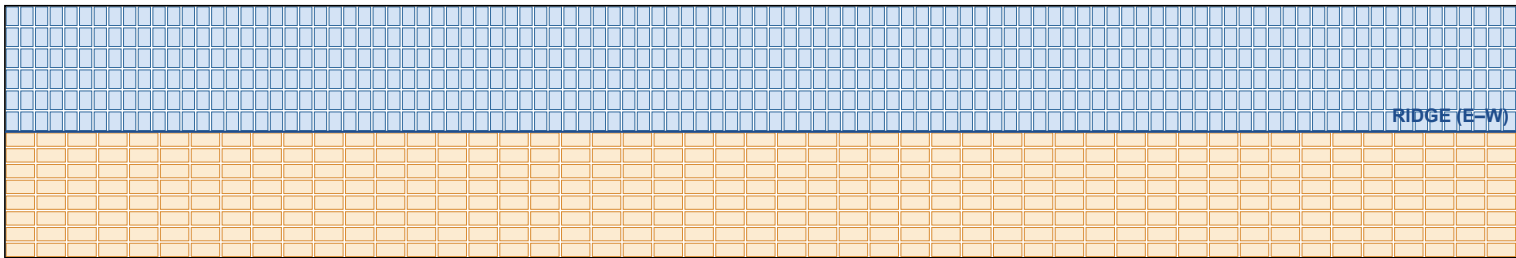

SOUTH FACE (efficient) — STP710S-D66 710W: 392 pcs (49×8 landscape)



LEGEND / QUANTITIES

Roof: 120×20 m · slope 11.27 m @27.5°

NORTH FACE:

STP450S-H48 450W · 618 pcs · 278 kWp

SOUTH FACE (efficient):

STP710S-D66 710W · 392 pcs · 49×8 landscape · 278 kWp

TOTAL hall: 1010 pcs $\approx$ 556 kWp

Fixing:

Fibre-cement hanger bolts + rails


C4 + C6: 1937 pcs $\approx$ 989 kWp (≤ 1 MW)

! Quantities/layout indicative — to confirm by survey and structural calc.

Working document; verification by an authorised designer.

SECTION A-A

1:150

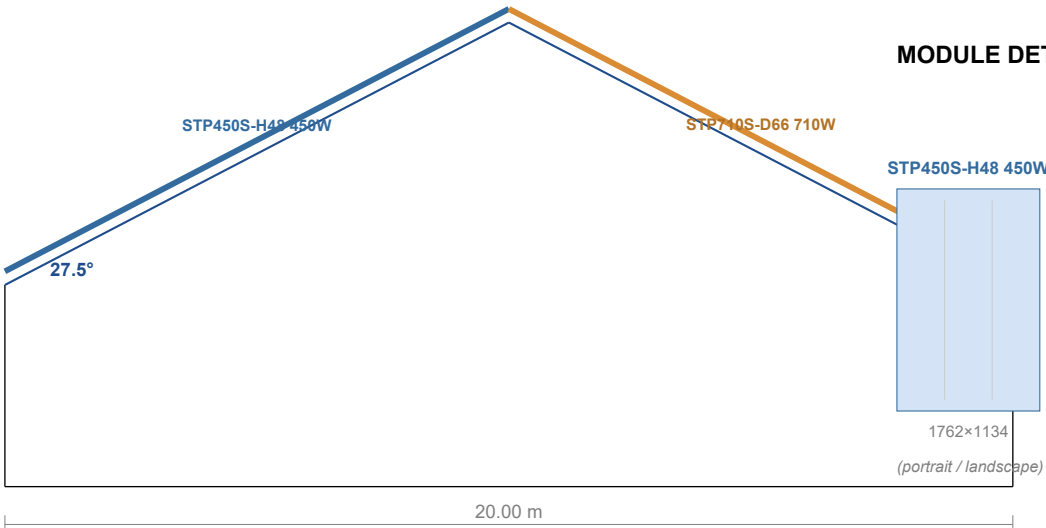

MODULE DETAIL (1:60)

STP450S-H48 450W

STP710S-D66 710W

1762×1134
(portrait / landscape)

2384×1303

CLIENT:

S.C. RED INTERNET SALES S.R.L.

PROJECT:

Autonomous PV plant — SMIS code 332037

≤ 1 MWp

Location: Albești (Sighișoara), Mureș County, RO

DRAWING:

HALL C4

PV module mounting plan

Phase: informative

Drawn: Checked:

SCALE:

1:600 / 1:150

DATE:

08.2026

FORMAT:

A3

SHEET:

M-01


PV-MODULMONTAGEPLAN — HALLE C4

Modulanordnung auf den 2 Dachflächen (effizient auf Süd) — installiert ≤ 1 MW, dachparallel

VERLEGEPLAN — MODULANORDNUNG

M 1:600


DACHFLÄCHE NORD — STP450S-H48 450W: 618 Stk (103×6 Hochformat)

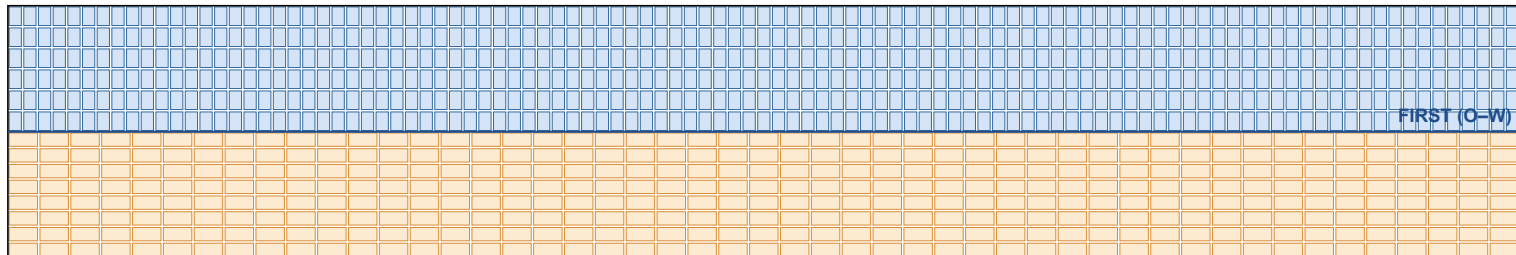

DACHFLÄCHE SÜD (effizient) — STP710S-D66 710W: 392 Stk (49×8 Querformat)

QUERSCHNITT A-A

1:150

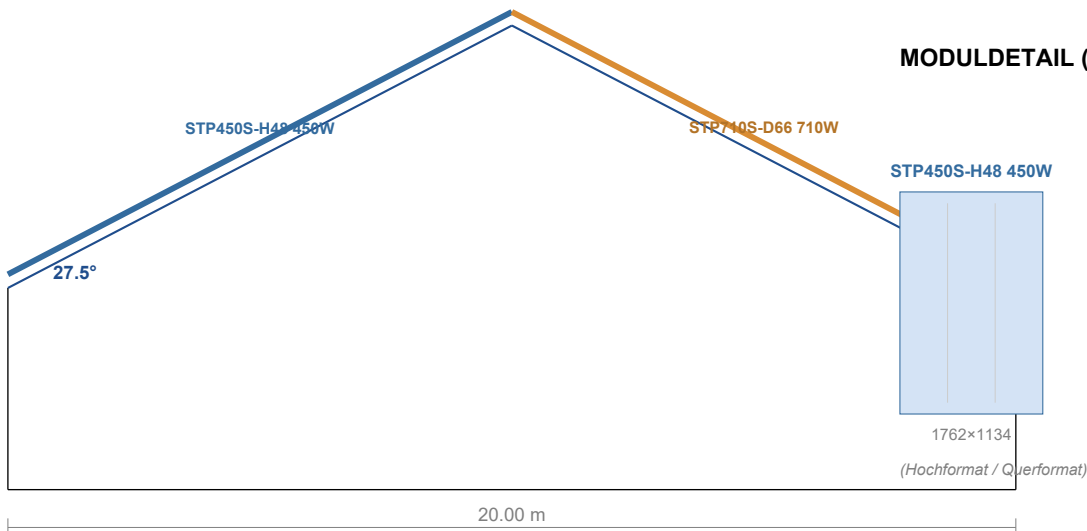

MODULDETAIL (1:60)

STP450S-H48 450W

1762×1134
(Hochformat / Querformat)

STP710S-D66 710W

2384×1303

N

LEGENDE / MENGEN

Dach: 120×20 m · Sparren 11,27 m @27,5°

DACHFLÄCHE NORD:

STP450S-H48 450W · 618 Stk · 278 kWp

DACHFLÄCHE SÜD (effizient):

STP710S-D66 710W · 392 Stk · 49×8 Querformat · 278 kWp

GESAMT Halle: 1010 Stk ≈ 556 kWp

Befestigung:

Faserzement-Stockschrauben + Schienen

C4 + C6: 1937 Stk ≈ 989 kWp (≤ 1 MW)

! Mengen/Anordnung Richtwerte — durch Aufmaß und Statik zu bestätigen.

Arbeitsdokument; Prüfung durch autorisierten Planer.

BAUHERR:

S.C. RED INTERNET SALES S.R.L.

PROJEKT:

Autonome PV-Anlage — SMIS-Code 332037

≤ 1 MWp

Standort: Albești (Schäßburg), Kreis Mureș

PLANINHALT:

HALLE C4

PV-Modulmontageplan

Phase: informativ

Erstellt: Geprüft:

MASSSTAB:

1:600 / 1:150

DATUM:

08.2026

FORMAT:

A3

BLATT:

M-01